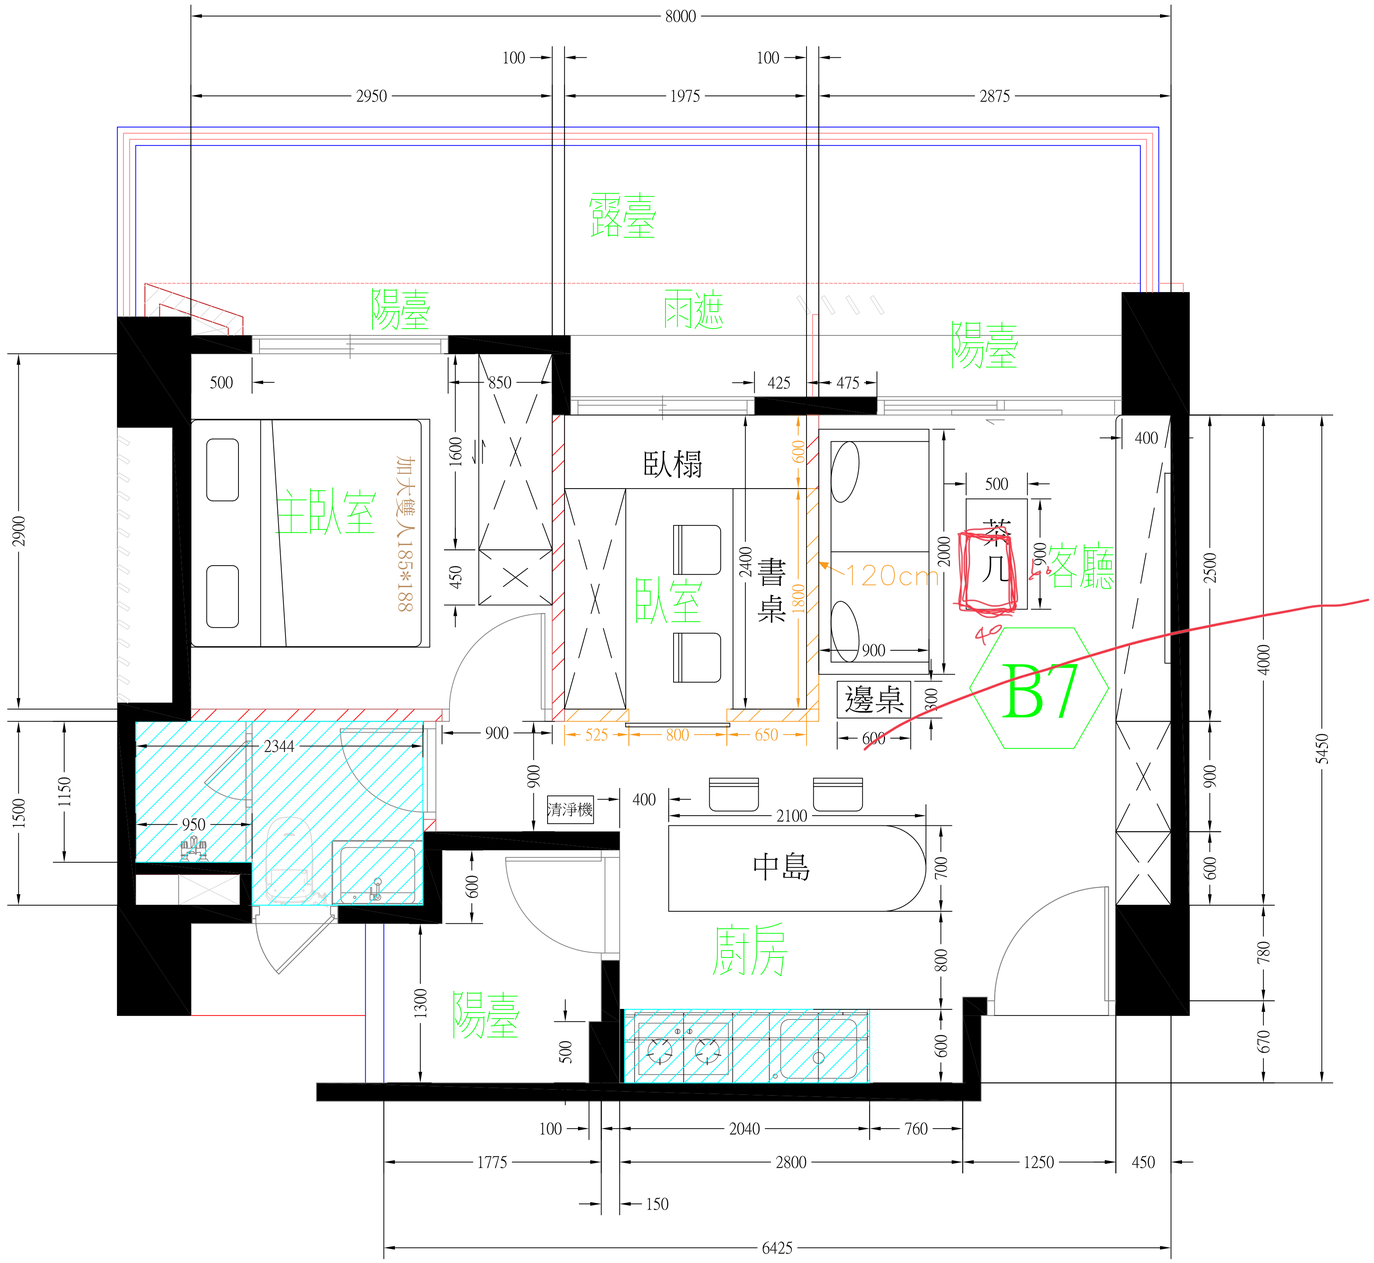

繹芯

空間設計
室内裝修
股份有限公司

案名: 林口王先生
圖名-平面配置圖
設計-Joel
繪圖-Com
比例-1:50(A3)
單位-mm
日期-2024/04/23
案號 PROUECT NO.
張號 SHEET NO.1
圖號 DRAWING NO.

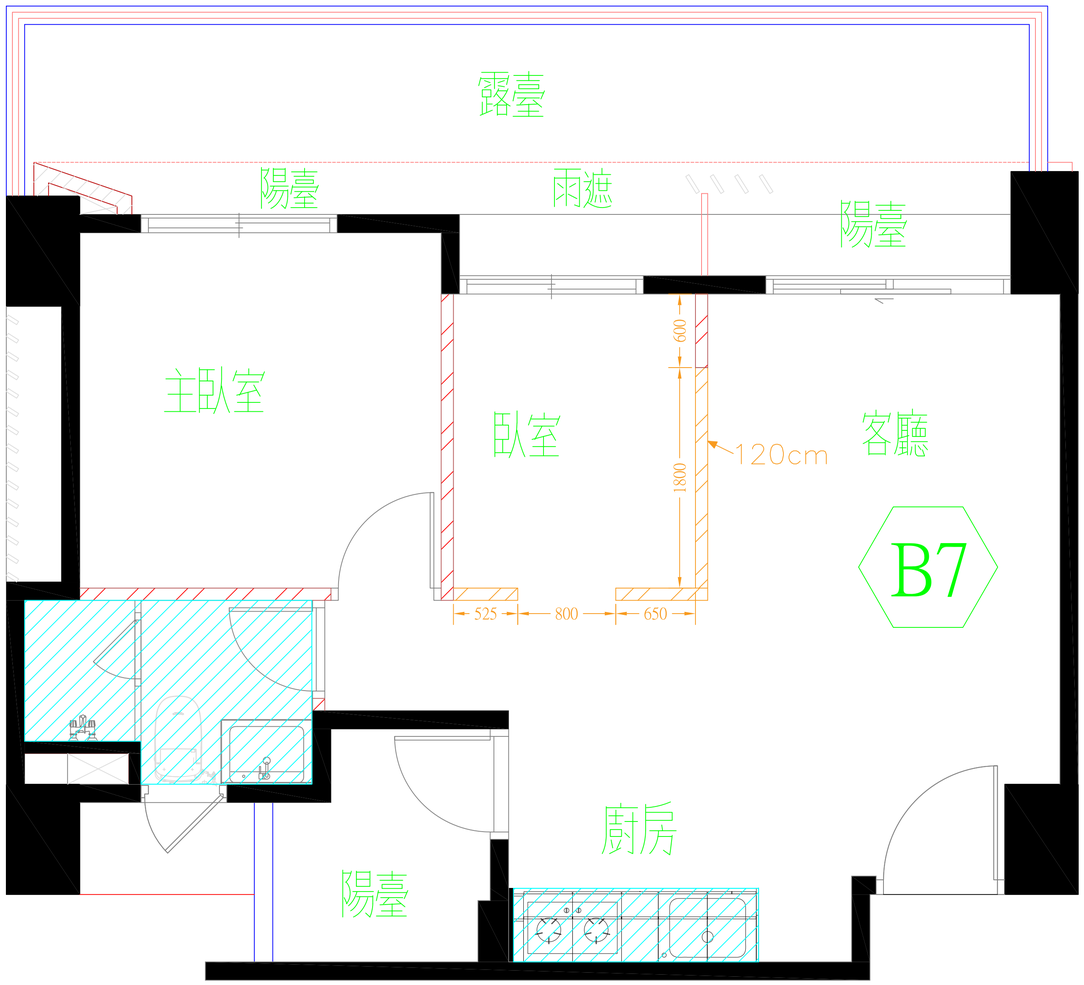

	客 變 項 目
1	退全室踢腳
2	退次臥門 門洞改為80公分寬移至中間(尺寸如圖)
3	退衛浴五金(衛生紙架、毛巾架、置物架)
4	退浴鏡
5	退全室室內地板
6	沙發背墻 窗戶進來60公分後改為120公分高矮墻(尺寸如圖)

繹芯

空間設計
室內裝修
股份有限公司

□ y
□□

案名: 林口王先生

圖名-平面配置圖
客變

設計-Joel

繪圖-Com

比例-1:50(A3)

單位-mm

日期-2024/04/23

案號
PROUECT NO.

張號
SHEET NO.1

圖號
DRAWING NO.

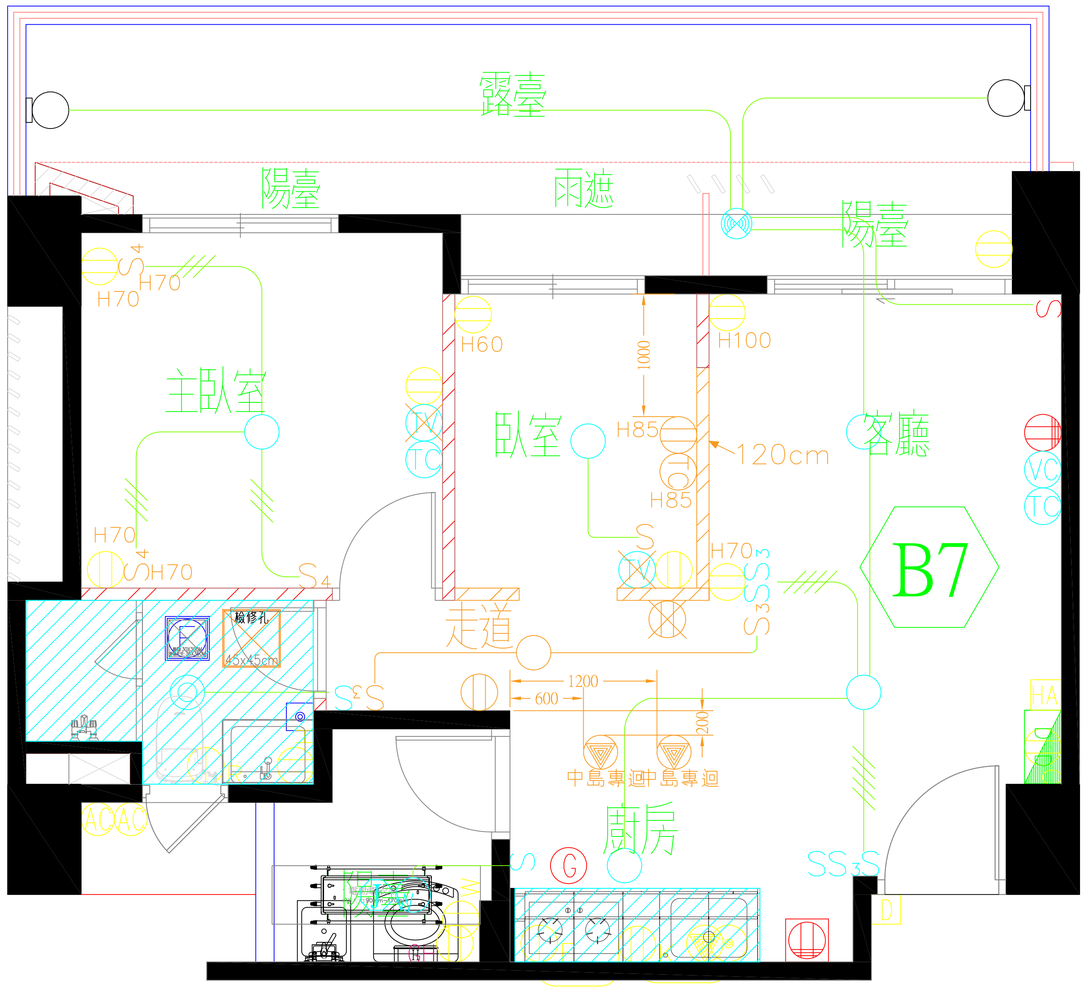

	客 變 項 目
1	主臥電燈改為4路開關 新開關做在另一側床頭
2	主臥床頭開關插座移到 高70公分處(橫式)
3	退主臥和次臥電視插座
4	次臥窗邊電話插座及資訊插座 移到沙發背墻
5	次臥門旁邊開關跟著門洞客變 右移 旁邊插座取消
6	次臥窗戶旁邊插座抬升到60公 分高
8	新增走道3路開關電燈迴路
9	新增兩組中島專迴 地面出線
10	三合一通風門右側牆 新增插座
11	沙發背墻 落地窗側插座改為100公分高 走道側插座改為70公分高

繹芯

空間設計
室內裝修
股份有限公司

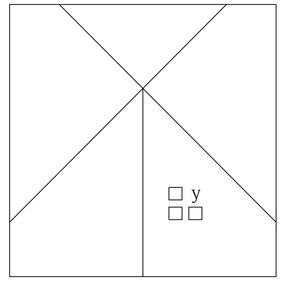

案名: 林口王先生

圖名-弱電電器
平面圖 客變

設計-Joel

繪圖-Com

比例-1:50(A3)

單位-mm

日期-2024/04/23

案號
PROUECT NO.

張號
SHEET NO.2

圖號
DRAWING NO.

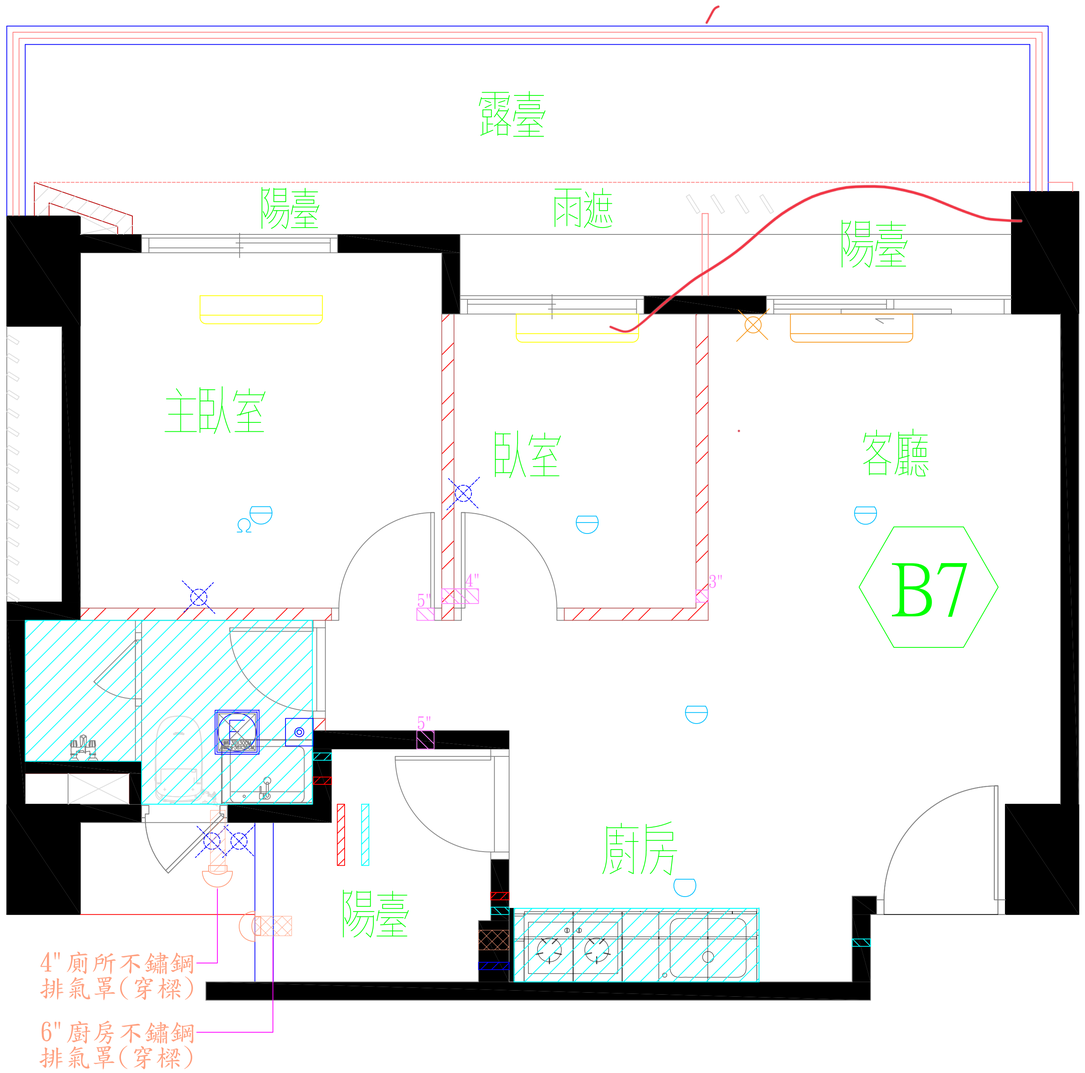

	客 變 項 目
1	客廳冷氣排水改至落地窗左上

繹芯

空間設計
室內裝修
股份有限公司

案名: 林口王先生

圖名-消防平面圖
客變

設計-Joel

繪圖-Com

比例-1:50(A3)

單位-mm

日期-2024/04/19

案號
PROUECT NO.

張號
SHEET NO.4

圖號
DRAWING NO.